
Sanitaire adapté PMR - plan coté R+1

ÉCHELLE 1:20 - COTES EN MÈTRES

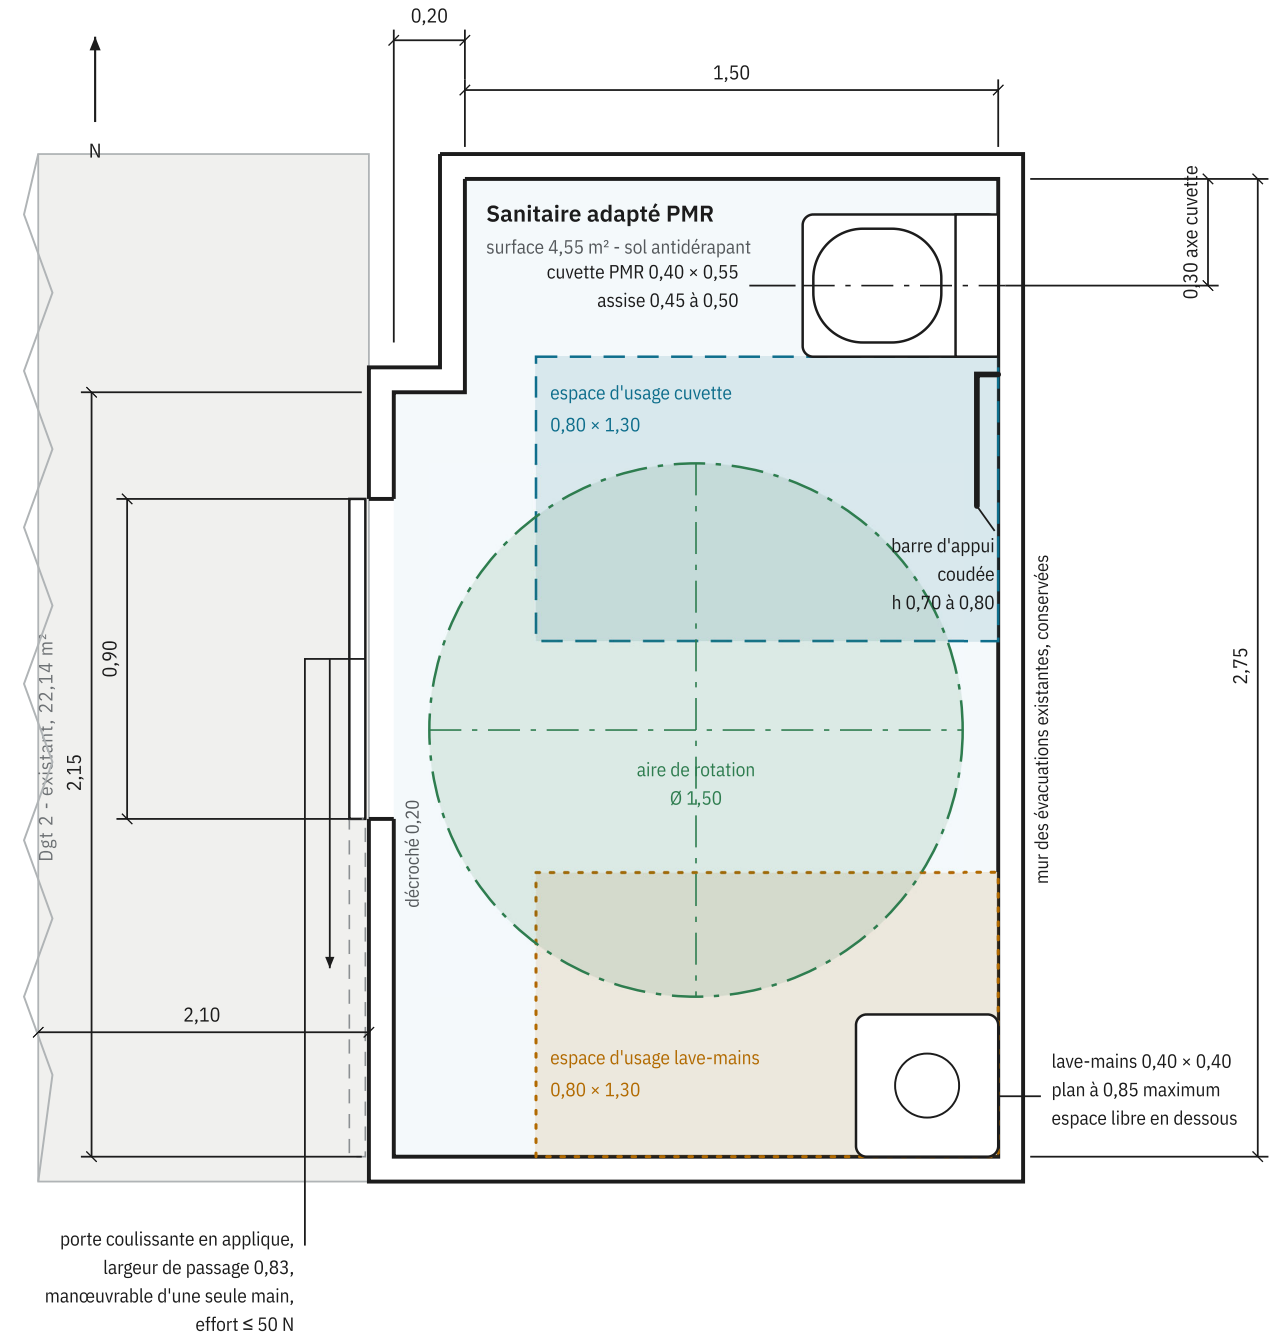

Aire de rotation Ø 1,50

Espace d'usage cuvette 0,80 × 1,30

Espace d'usage lave-mains 0,80 × 1,30

Cotes en mètres, cotes intérieures finies. Zones tramées : voir légende.

Réseaux d'évacuation existants conservés.

Sanitaire adapté PMR - plan coté R+1 Création d'un cabinet d'aisances adapté - dossier d'accessibilité ERP	**SCI Casa Artlia** 1B Ruelle des Jardins, 01210 Ferney-Voltaire Parcelle AE 247 Maître d'ouvrage : Lucian Stuparu	Échelle **1:20** Format A4 portrait Date 25/07/2026 Indice A